



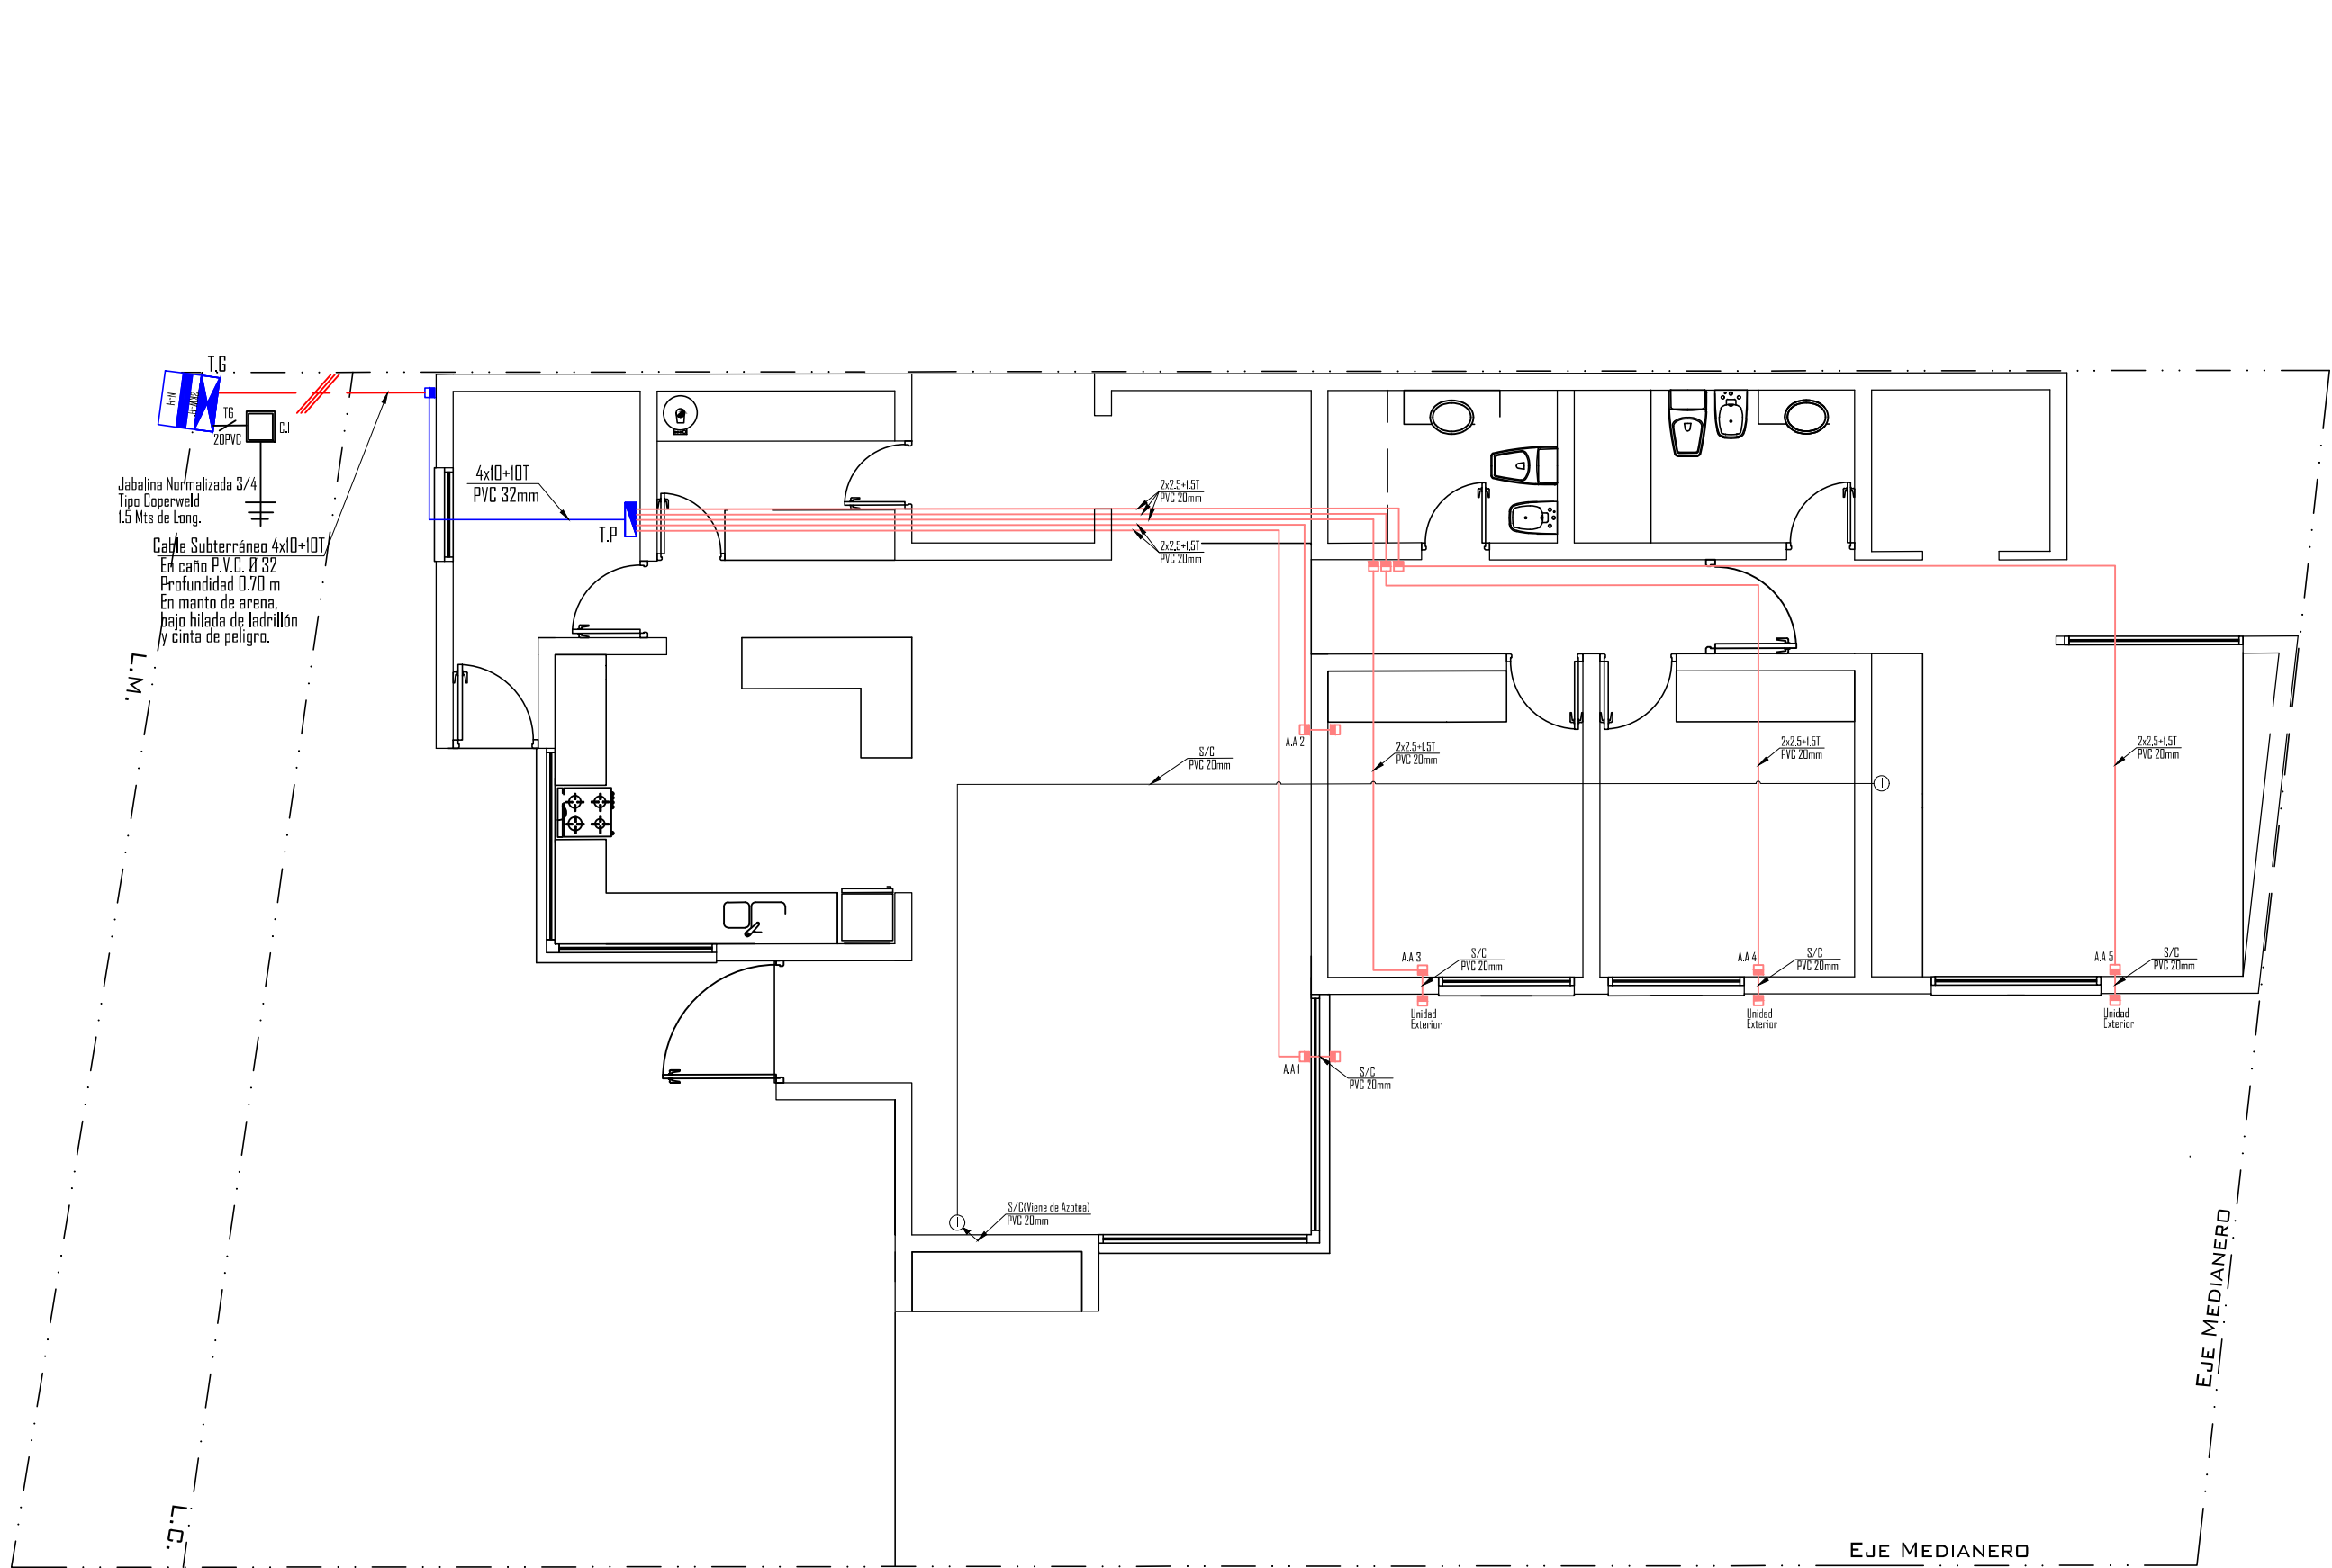


PLANTA A.A y BT

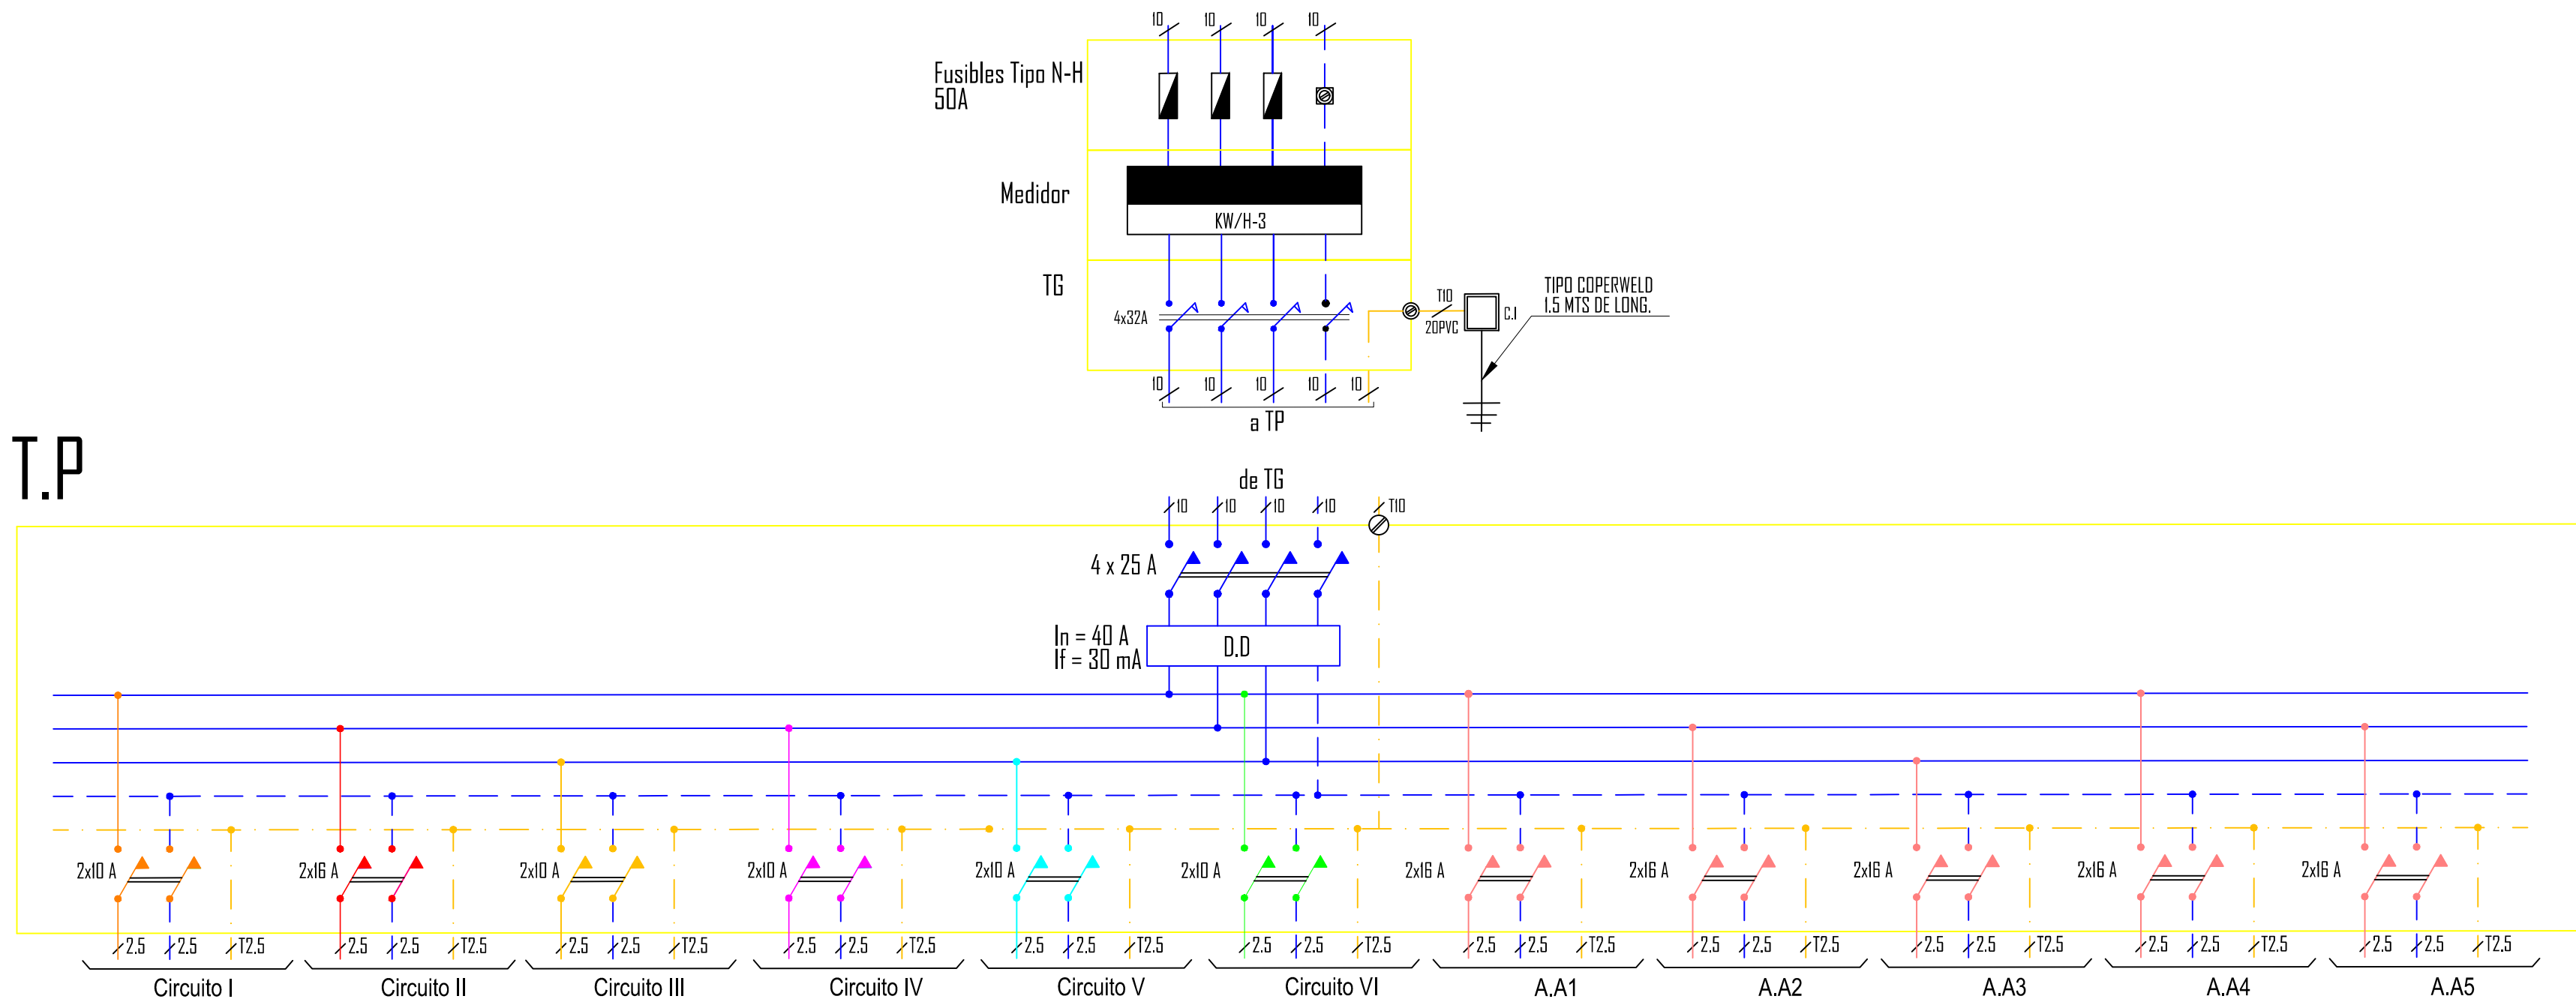


COMPUTO DE BOCAS PB							
Designación	Circuito I	Circuito II	Circuito III	Circuito IV	Circuito V	Circuito VI	BOCAS
Luces x 30w	7	8	8	9	14	10	56
Tomas x 150w	3	6	4	6	-	4	23
Sub. Total	10	14	12	15	14	14	Total: 79
Potencia(W)	330	420	630	330	420	630	2.9 Kw

CALCULO DE POTENCIA A.A	
Potencia	5000 w
5 kw	3500 w
5000 w al 70%	3.5 kw

Potencia Total: 2.9Kw + 3.5Kw= 6.4Kw

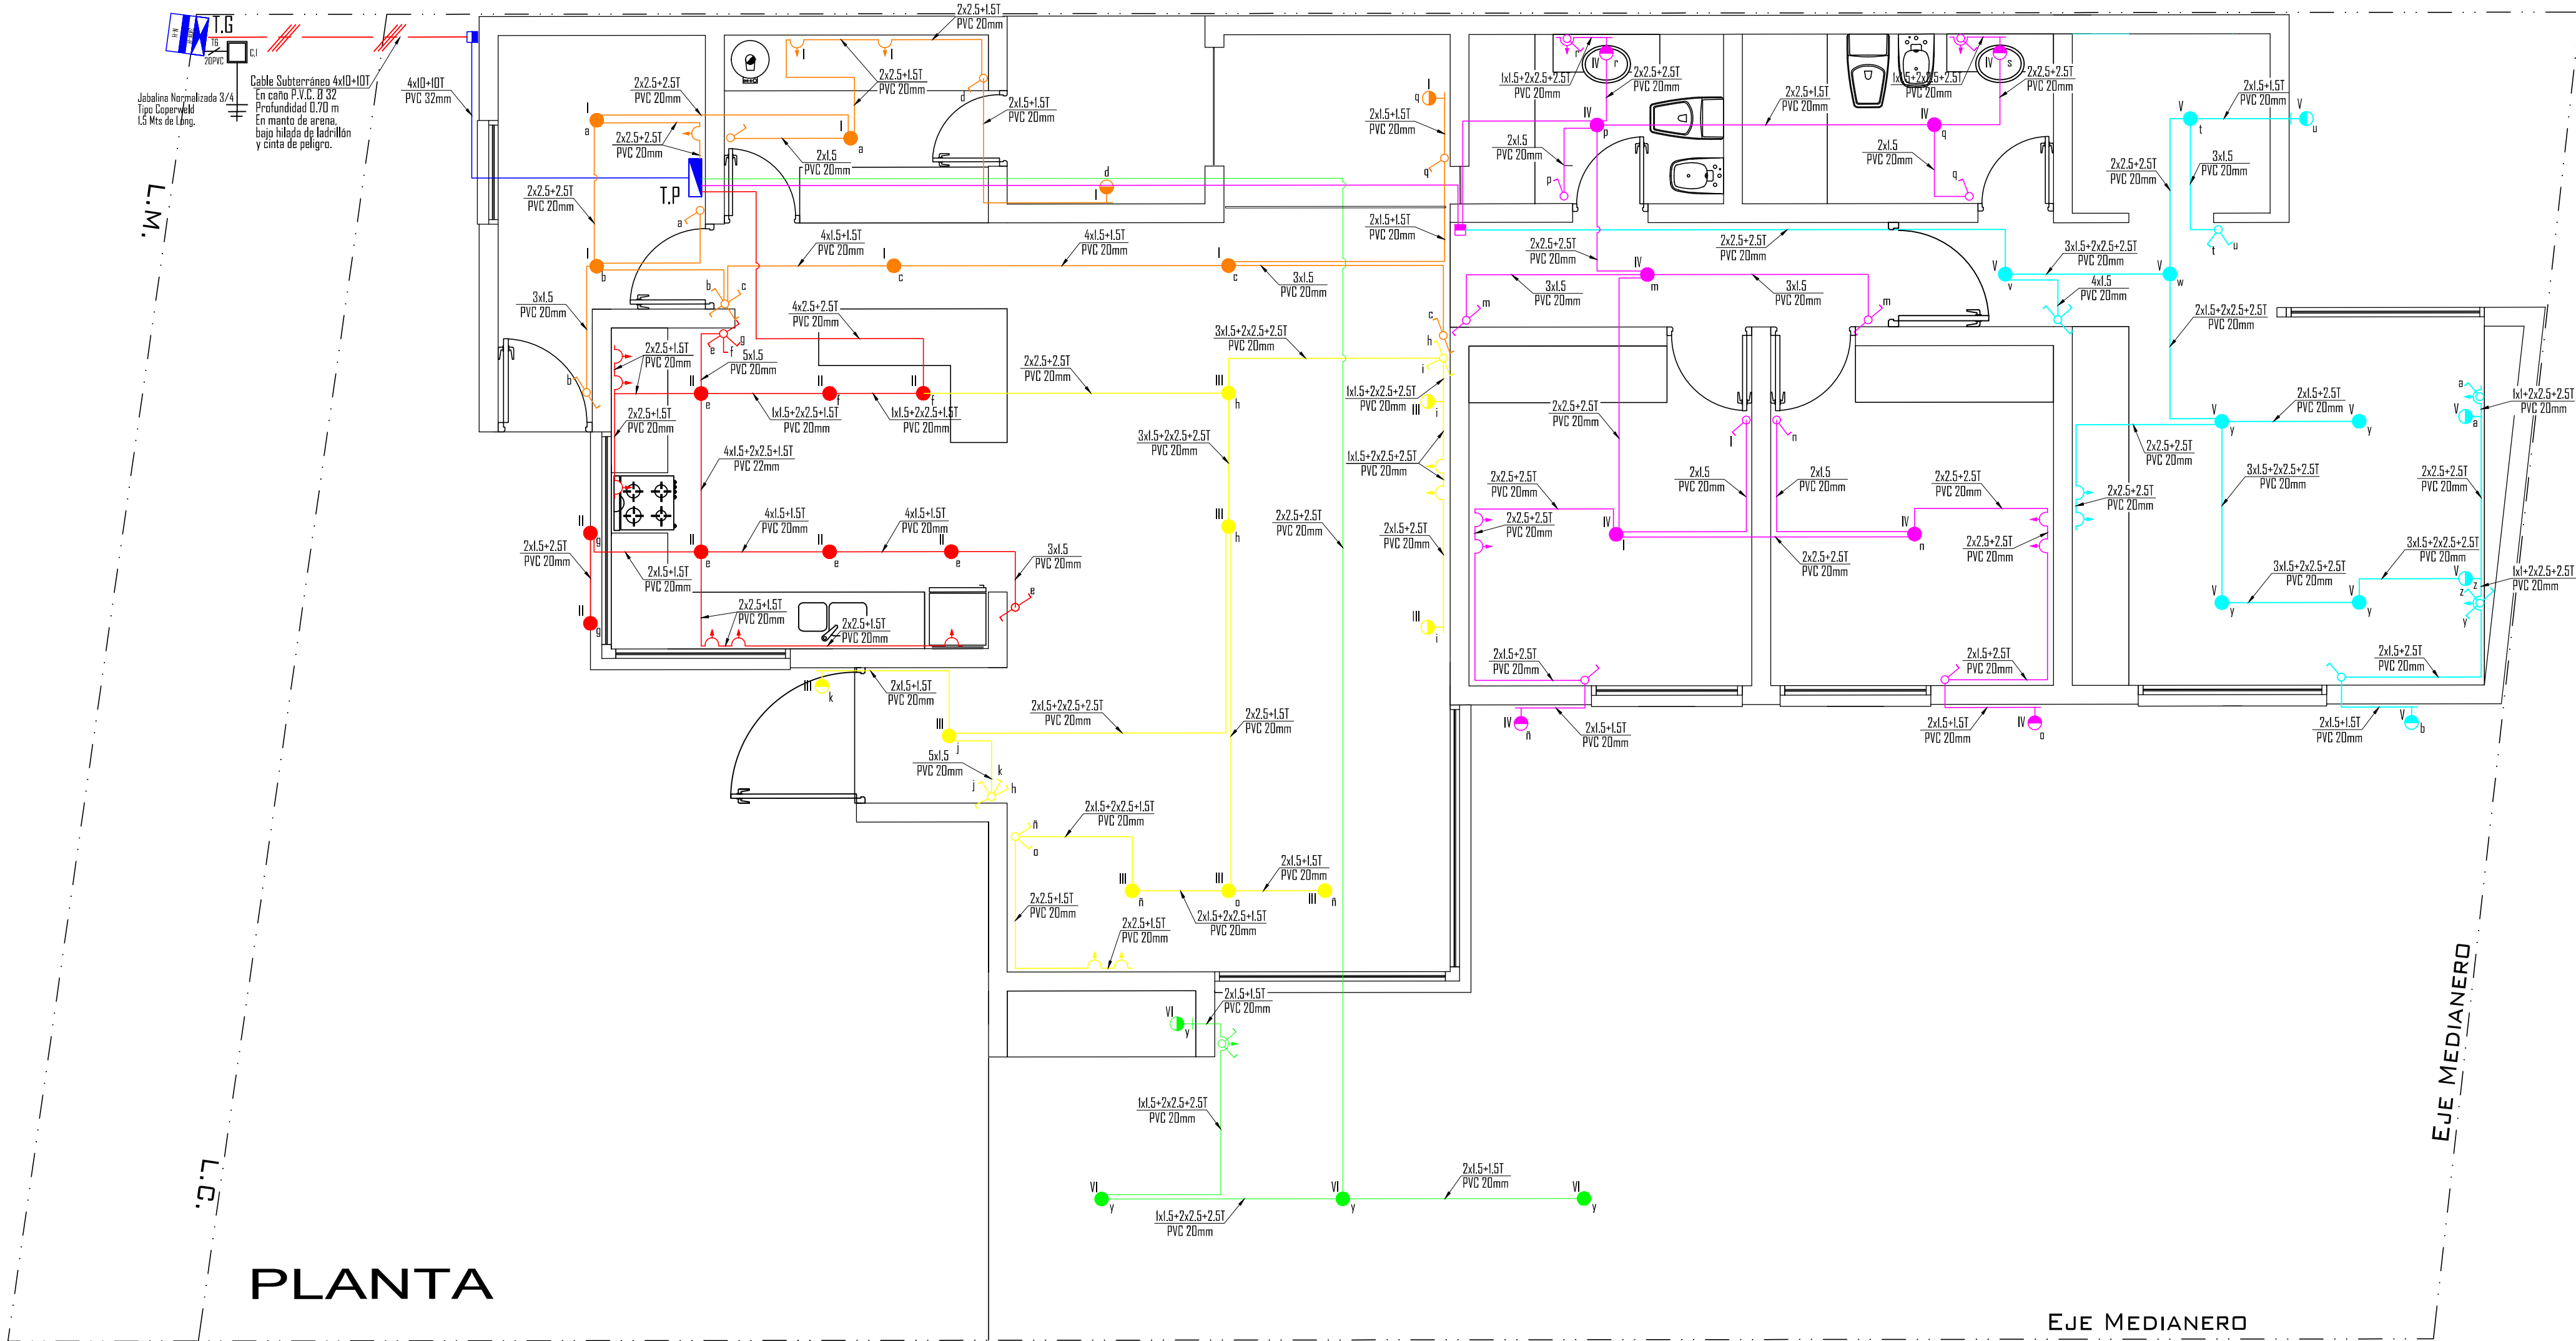

PLANTA

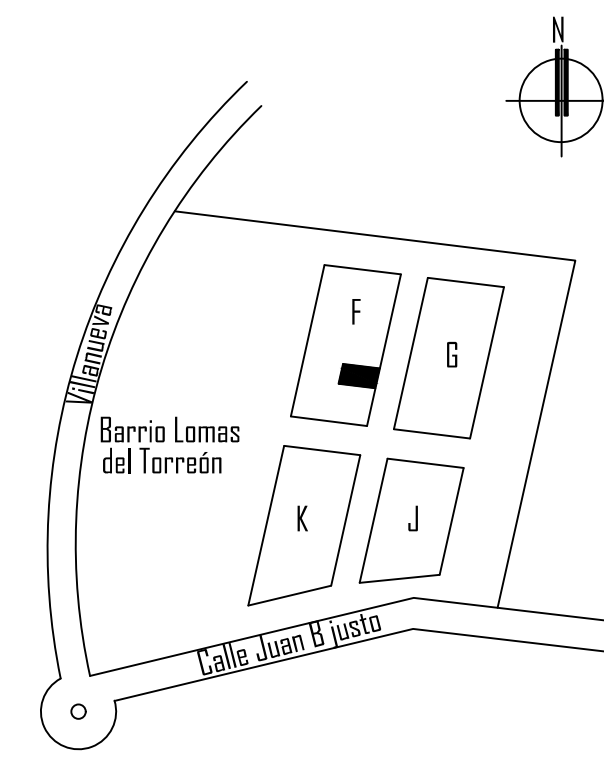NUEVA		INSTALACIÓN ELÉCTRICA	
OBRA: NUEVA DESTINO: Vivienda Unifamiliar UBICACIÓN: Barrio Lomas del Torreon-M F Lote II Gral. Gutierrez. Maipú. Mza. PROPIETARIO: Fideicomiso Lomas del Torréon .Salvago Argentina .SRL. DOMICILIO: Barrio Lomas del Torreon-M F Lote II Gral. Gutierrez. Maipú. Mza. POSEEDOR: Eliana Paula Moyano y Damián Hector Spotti			
FIRMA PROPIETARIO		SUP. CUR. : 160.04 M2 SUP. Sem Lab. : 13.50 M2 SUP. PATIOS: 161.58 M2	
PLANTA / TABLEROS		ESC. 1:50	I
TIPO : TRIFASICO		PADRON MUNICIPAL	15.953
		EXPEDIENTE N°:	13.796/2026
		PROYECTO / CALCULO INST. ELECTRICA Arg. Martin Lesack DOMICILIO: San Gabriel 105-Saday cruz-Mendoza	
		CATEG. A MAT. 2353	
		DIRECCION TECNICA INST. ELECTRICA Arg. Martin Lesack DOMICILIO: San Gabriel 105-Saday cruz-Mendoza	
		CATEG. A MAT. 2353	
EJECUCION INST. ELECTRICA		POR ADMINISTRACION A CARGO DEL PROPIETARIO	
VºBº ÁREA TÉCNICA		VISACION FINAL	
VºBº JEFE DE ÁREA			